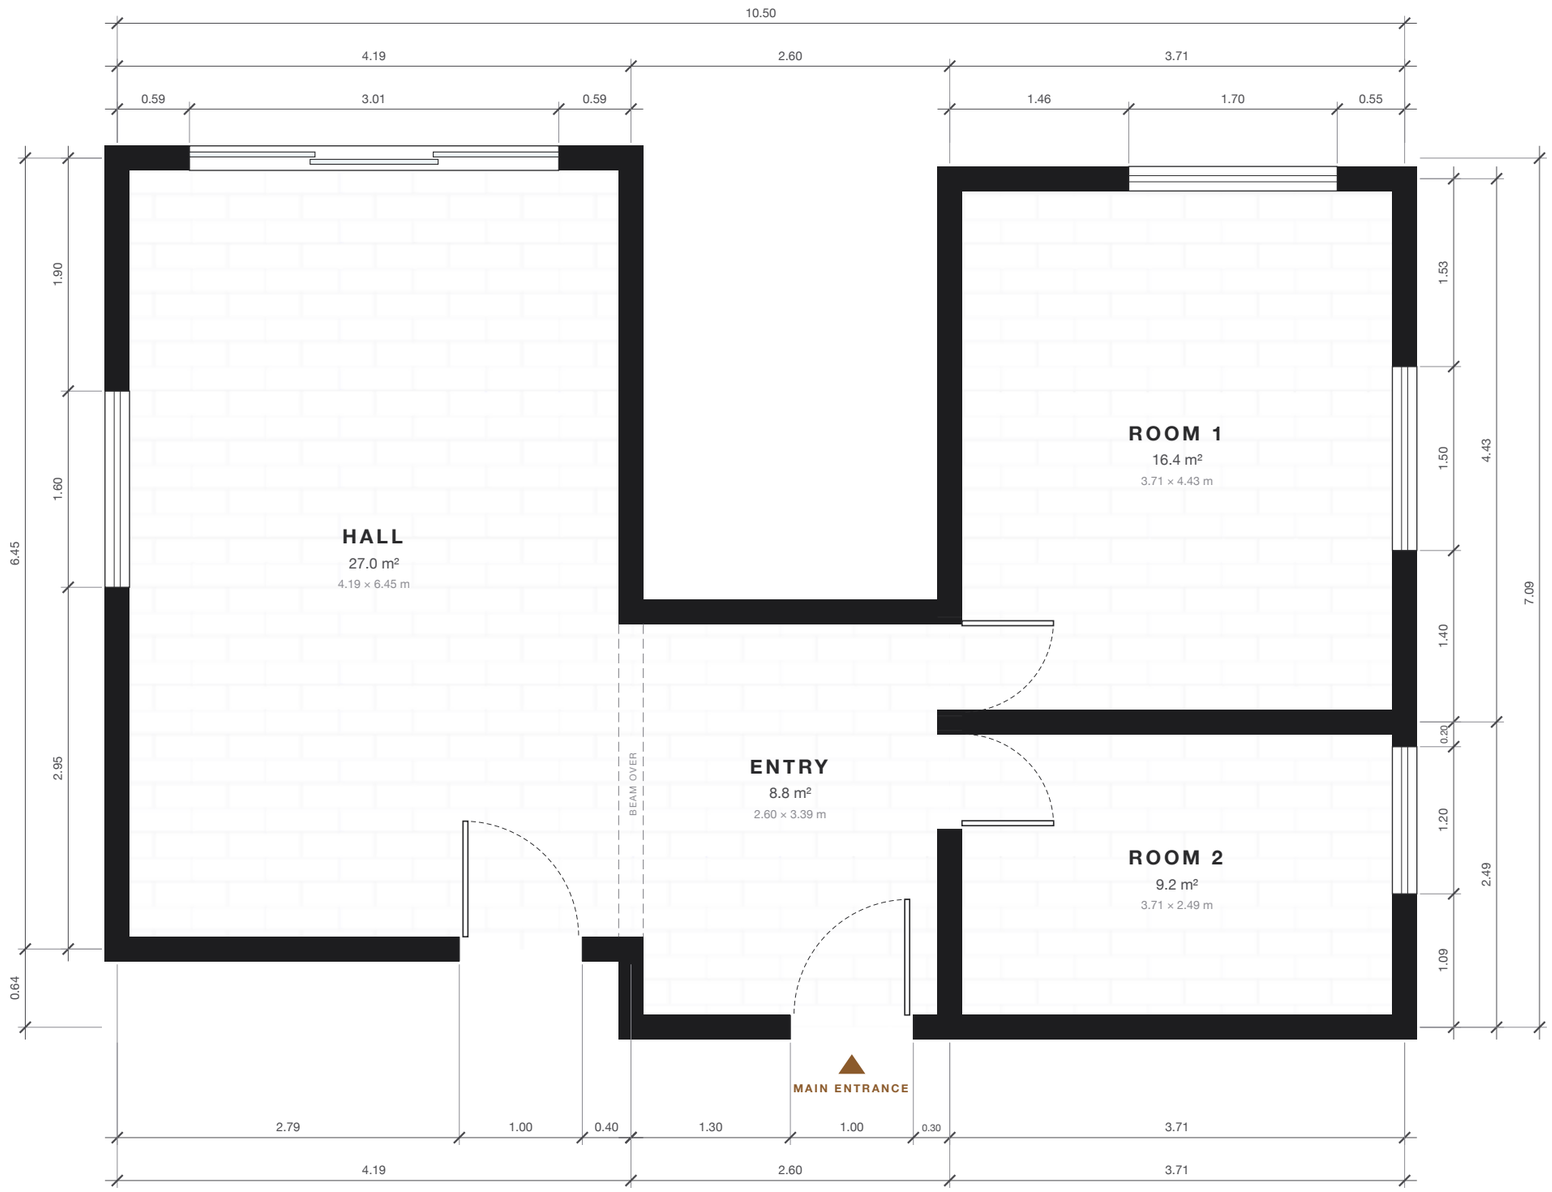


THE OFFICE

v2.0

Ground floor plan · existing layout

AREA SCHEDULE

Hall	4.19 × 6.45 m	27.0 m²
Entry	2.60 × 3.39 m	8.8 m²
Room 1	3.71 × 4.43 m	16.4 m²
Room 2	3.71 × 2.49 m	9.2 m²
Total		**61.5 m²**

LEGEND

- Wall, 20 cm
- Window
- Glass door, 3 panels
- Door and swing
- Overhead beam

NOTES

Dimensions in metres, to wall centre lines.
Clear ceiling height 3.00 m; gypsum drop at 2.72 m around each room.
Window sizes estimated from site photos.
Verify all dimensions on site.

SCALE 1:50 @ A3

0 1 2 3 4 m

DRAWING	SCALE
A-101	1:50
DATE	**REVISION**
10 Nov 2026	01